

RODINNÝ DOM – Situácia 1:200

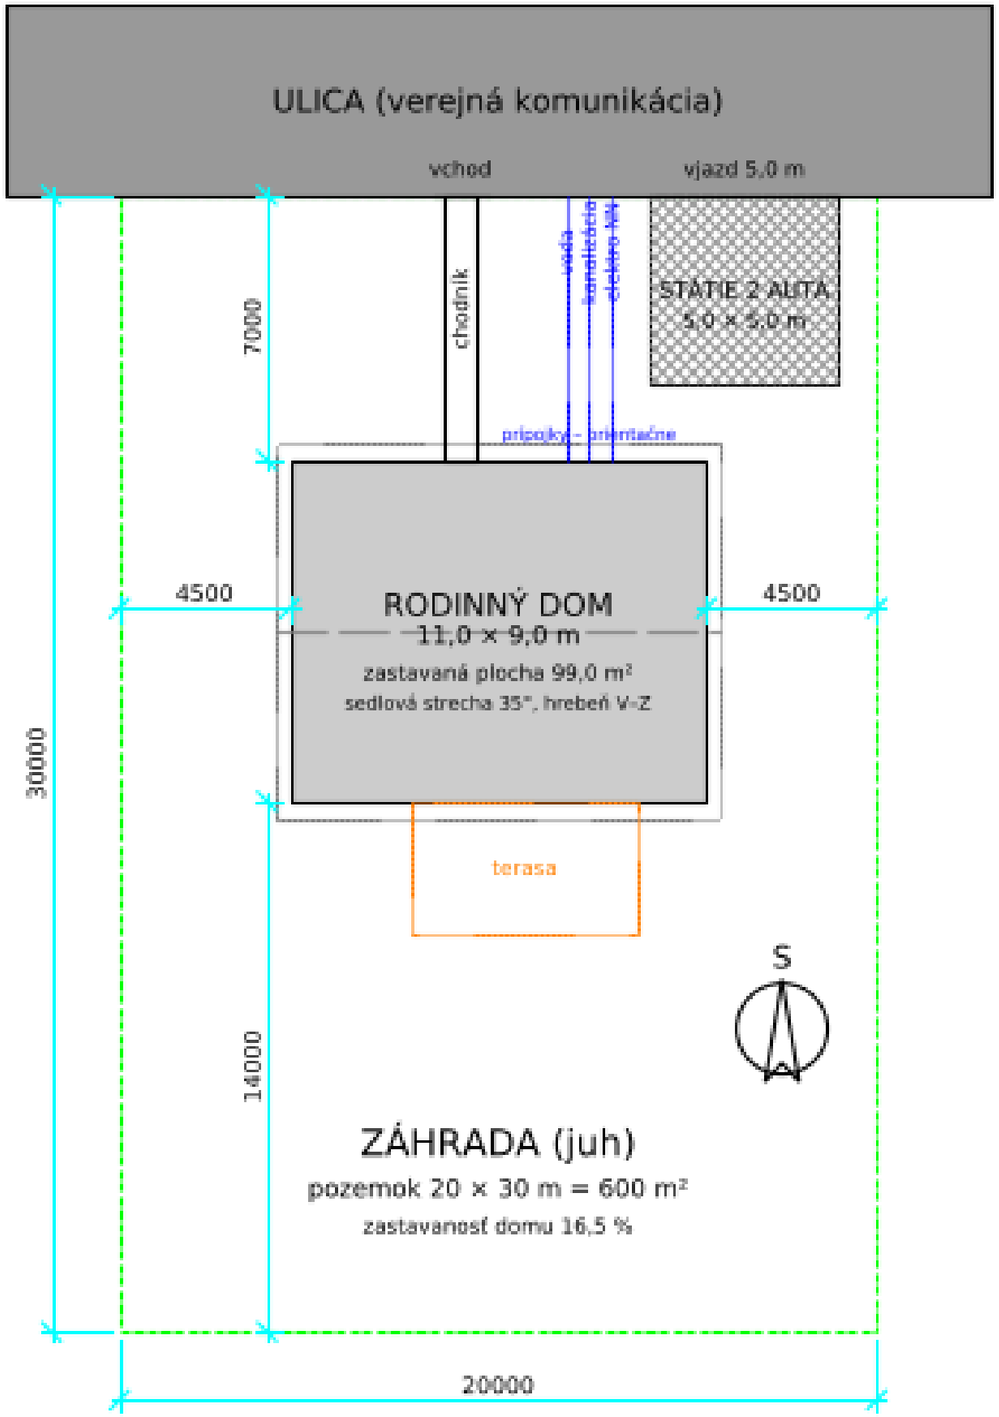

SITUÁCIA

RODINNÝ DOM – Základy

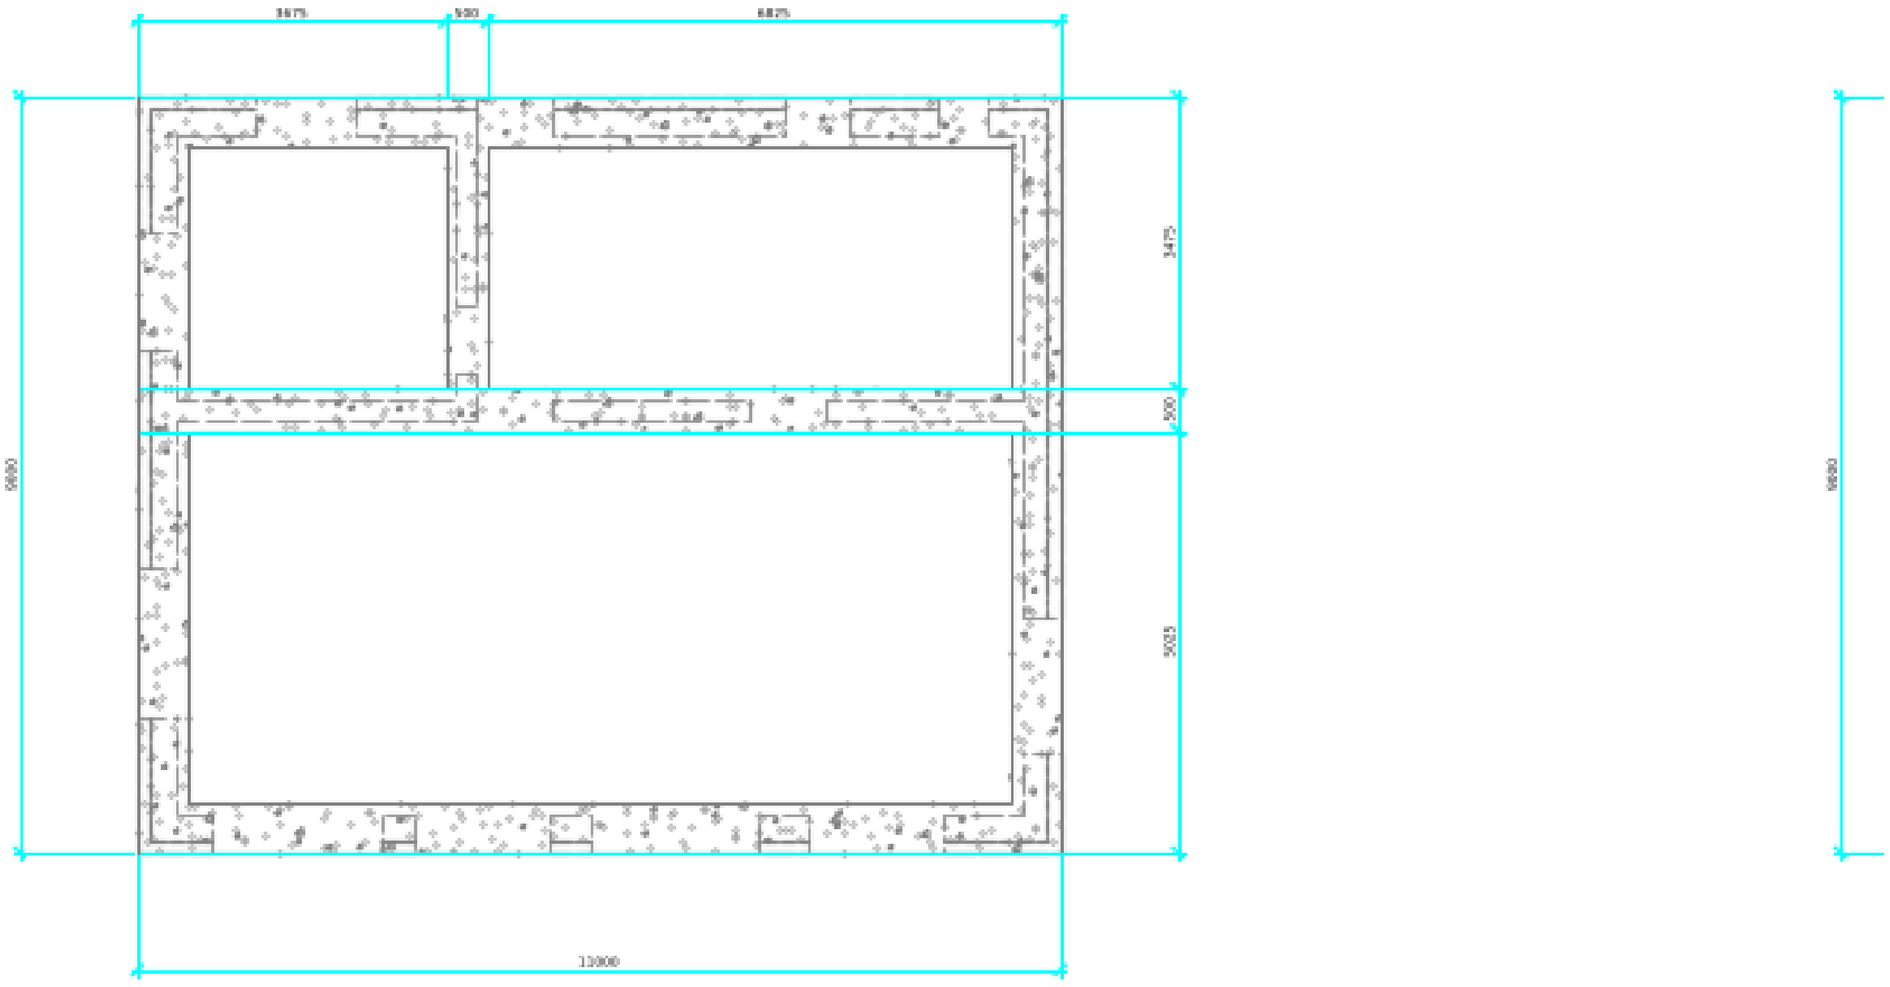

Základové pásy ZB: obvodové š. 600, vnútorné nosné š. 580


Základová škára -1.300 (1.0 m pod terénom, nepremŕzavá hĺbka)

Trieda betónu, výstuž a únosnosť zeminy – podľa statiky


a inžinierskogeologického prieskumu (radónové riziko I)

ZÁKLADY
M 1:50


RODINNÝ DOM – Pôdorys 1.NP

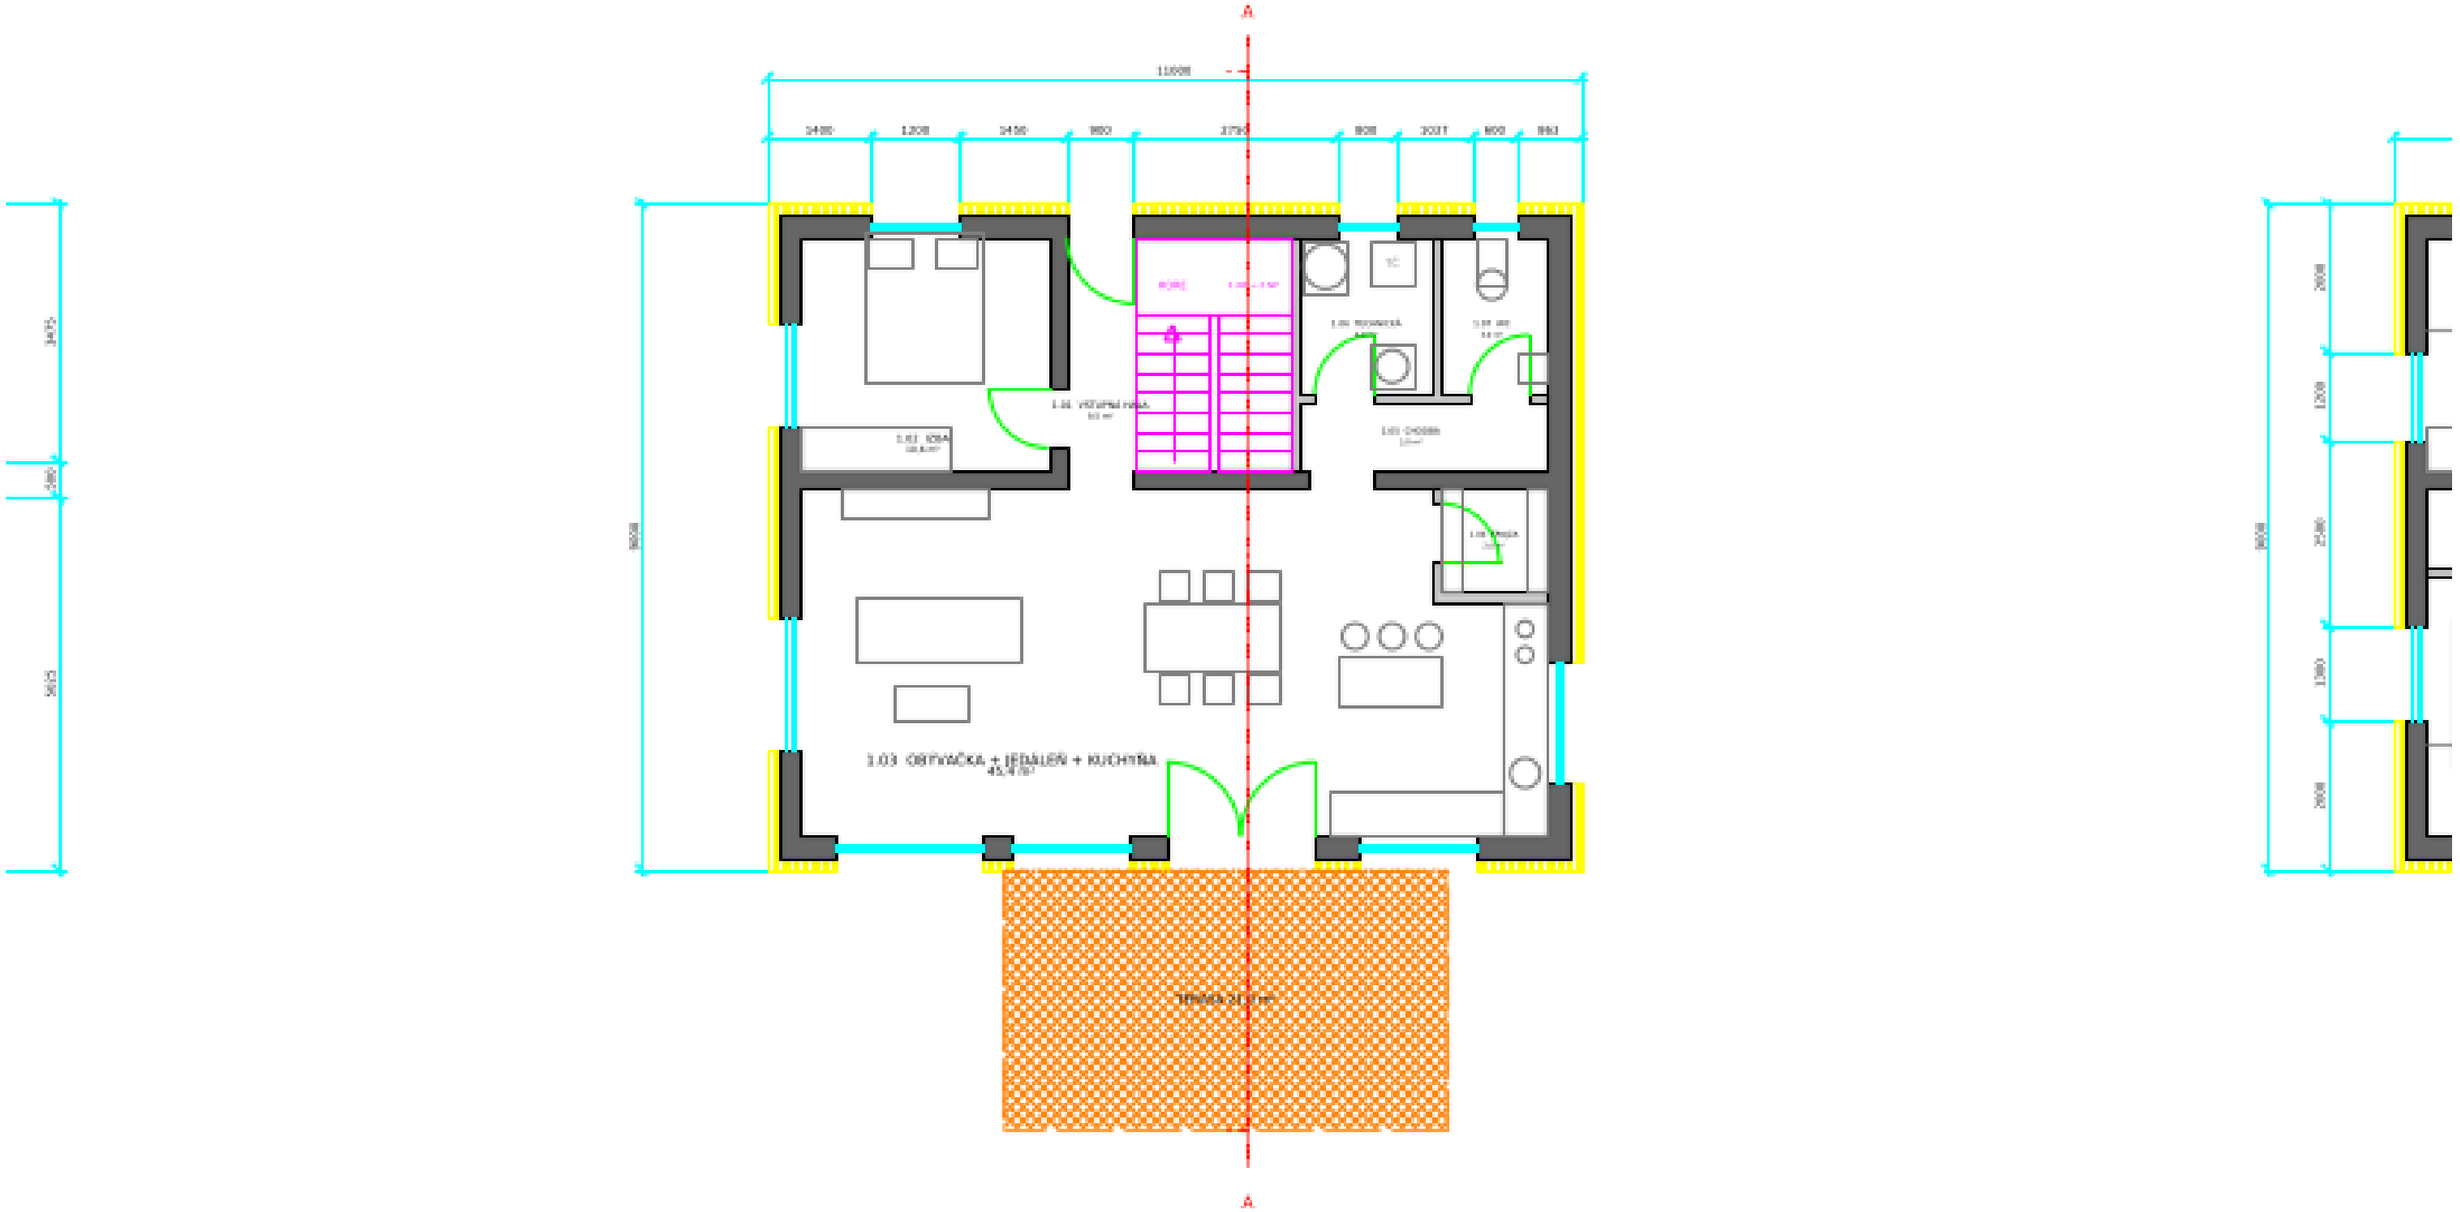

PÔDORYS 1.NP
M 1:50

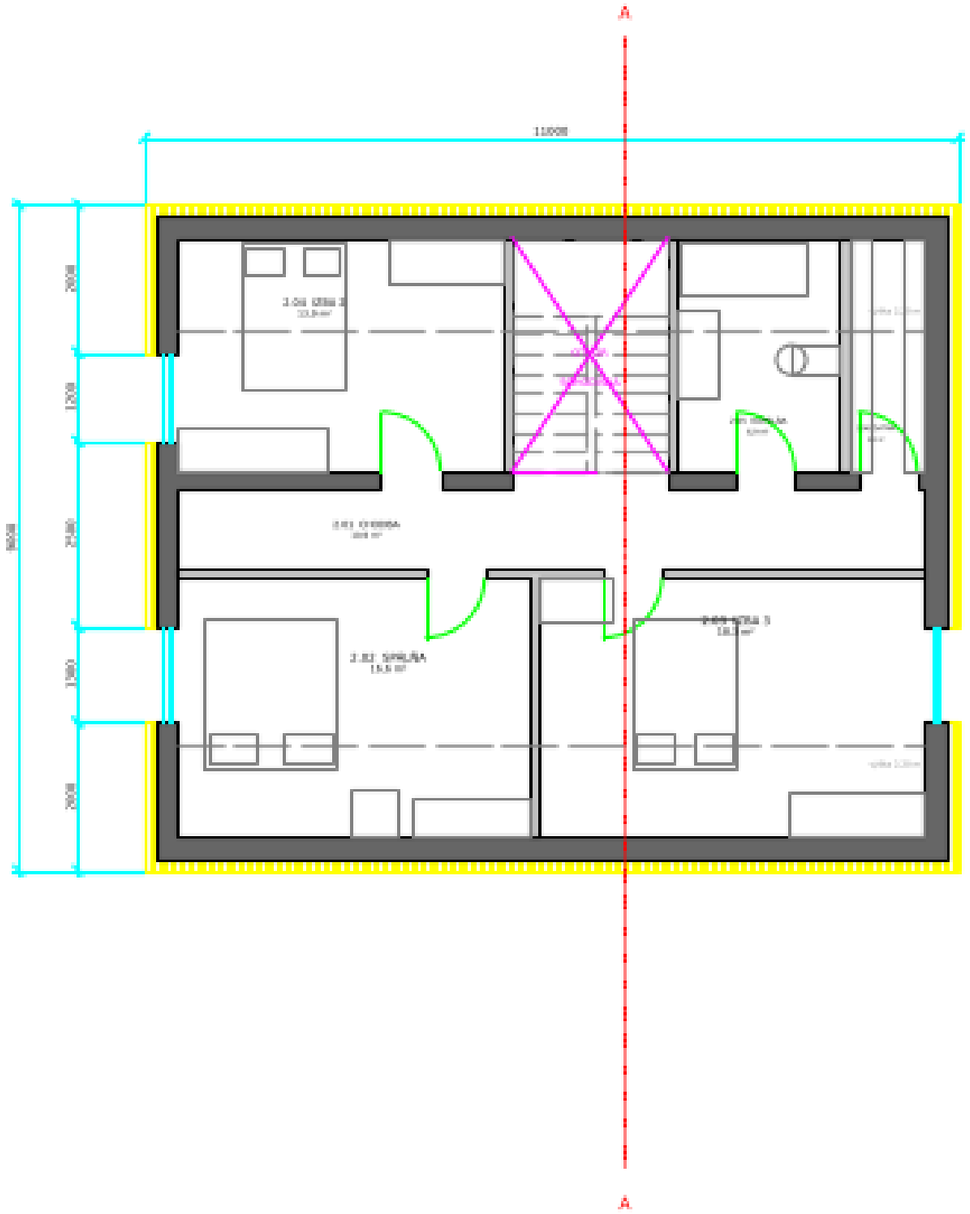


PÔDORYS 2.NP – PODKROVIE
M 1:50

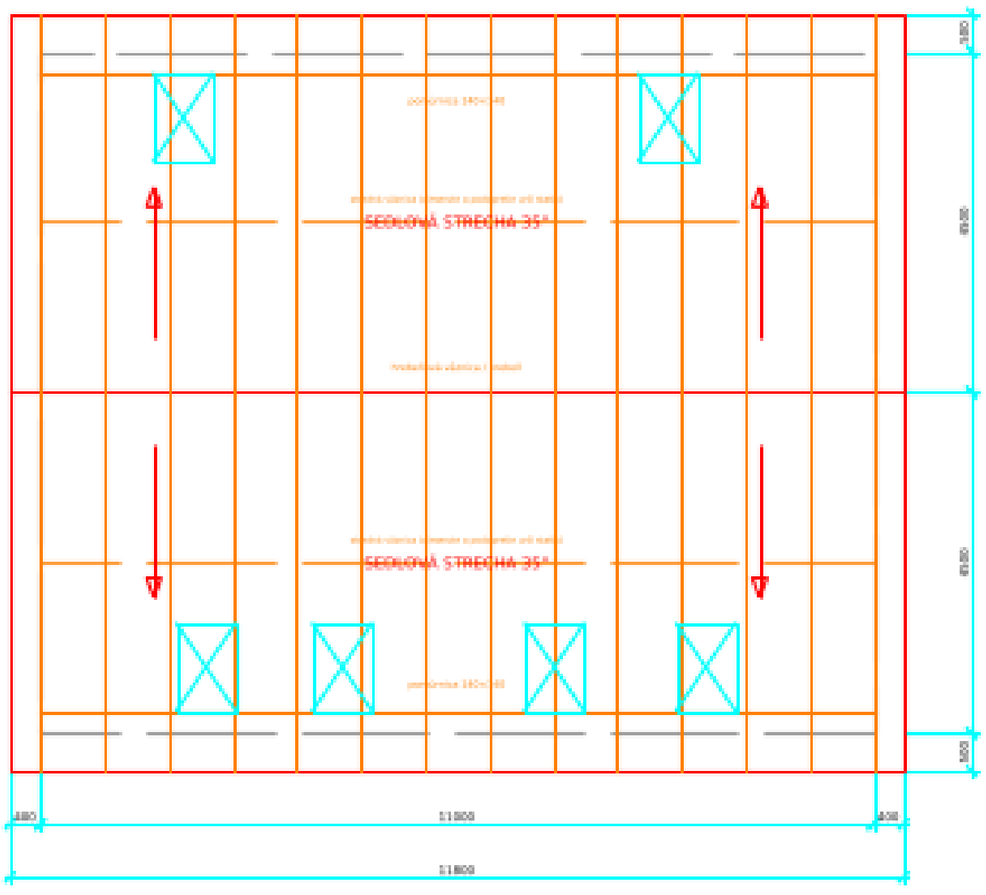

PÔDORYS STRECHY – SCHÉMA KROVU


M 1:50

RODINNÝ DOM – Rez A–A

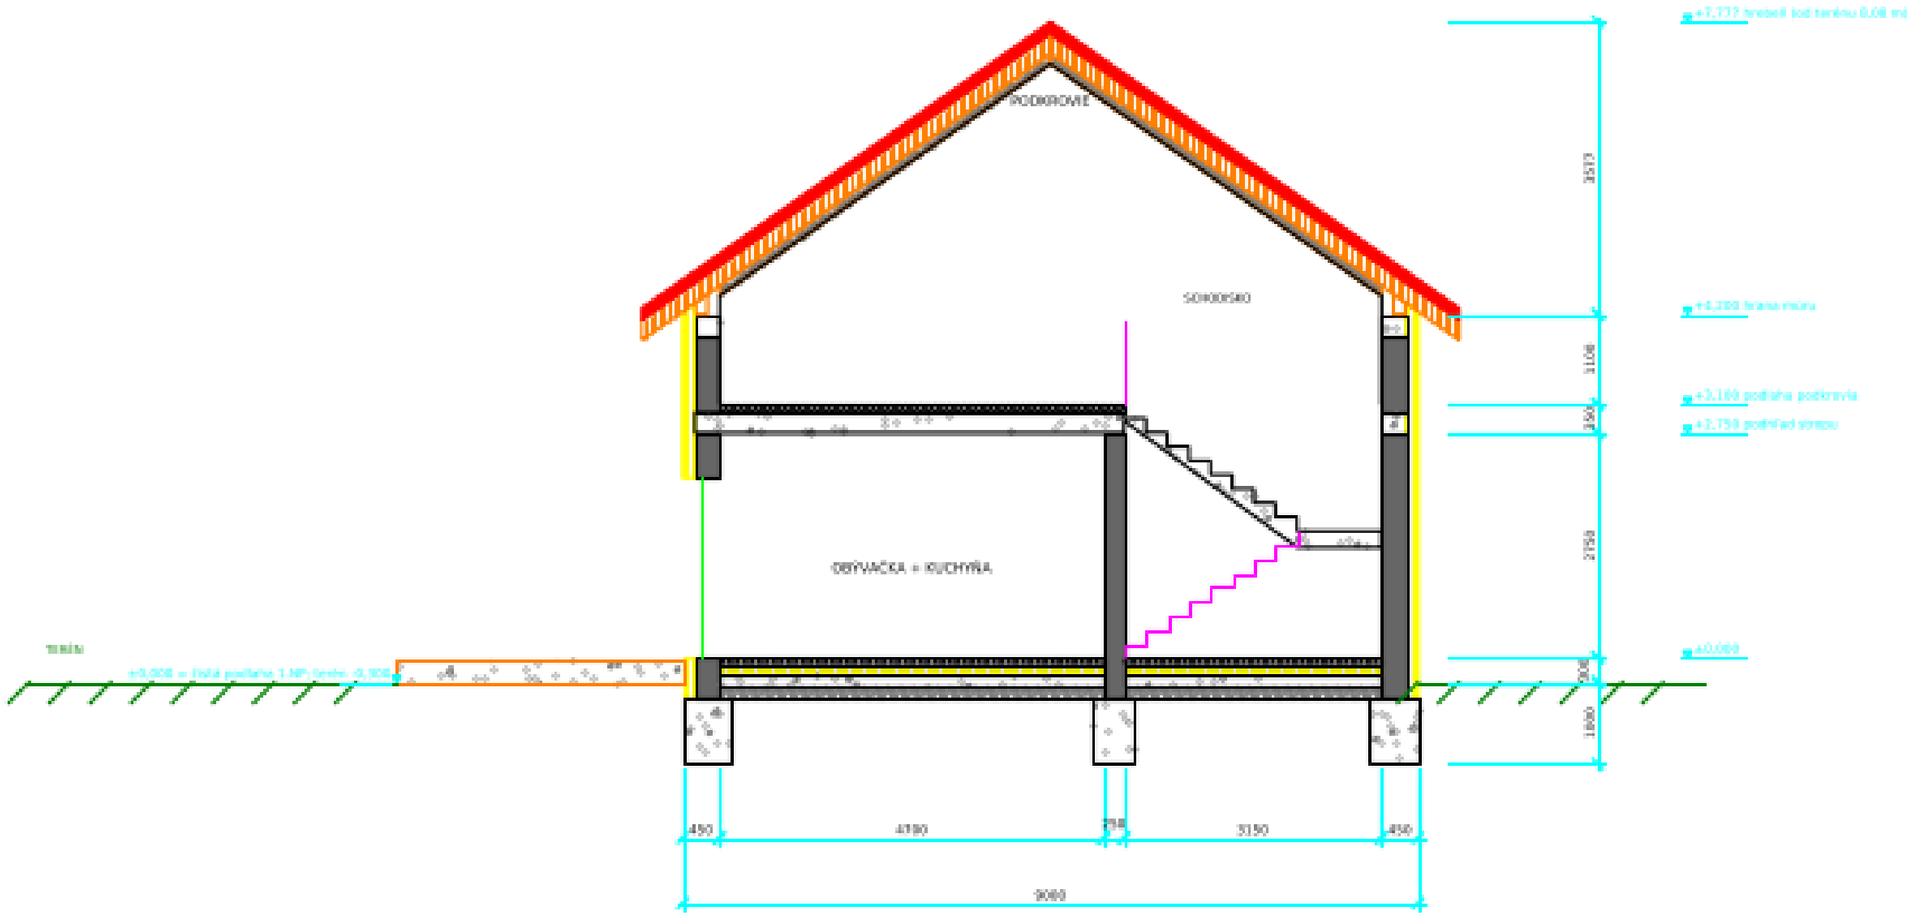


REZ A–A
M 1:50

RODINNÝ DOM – Pohľad južný

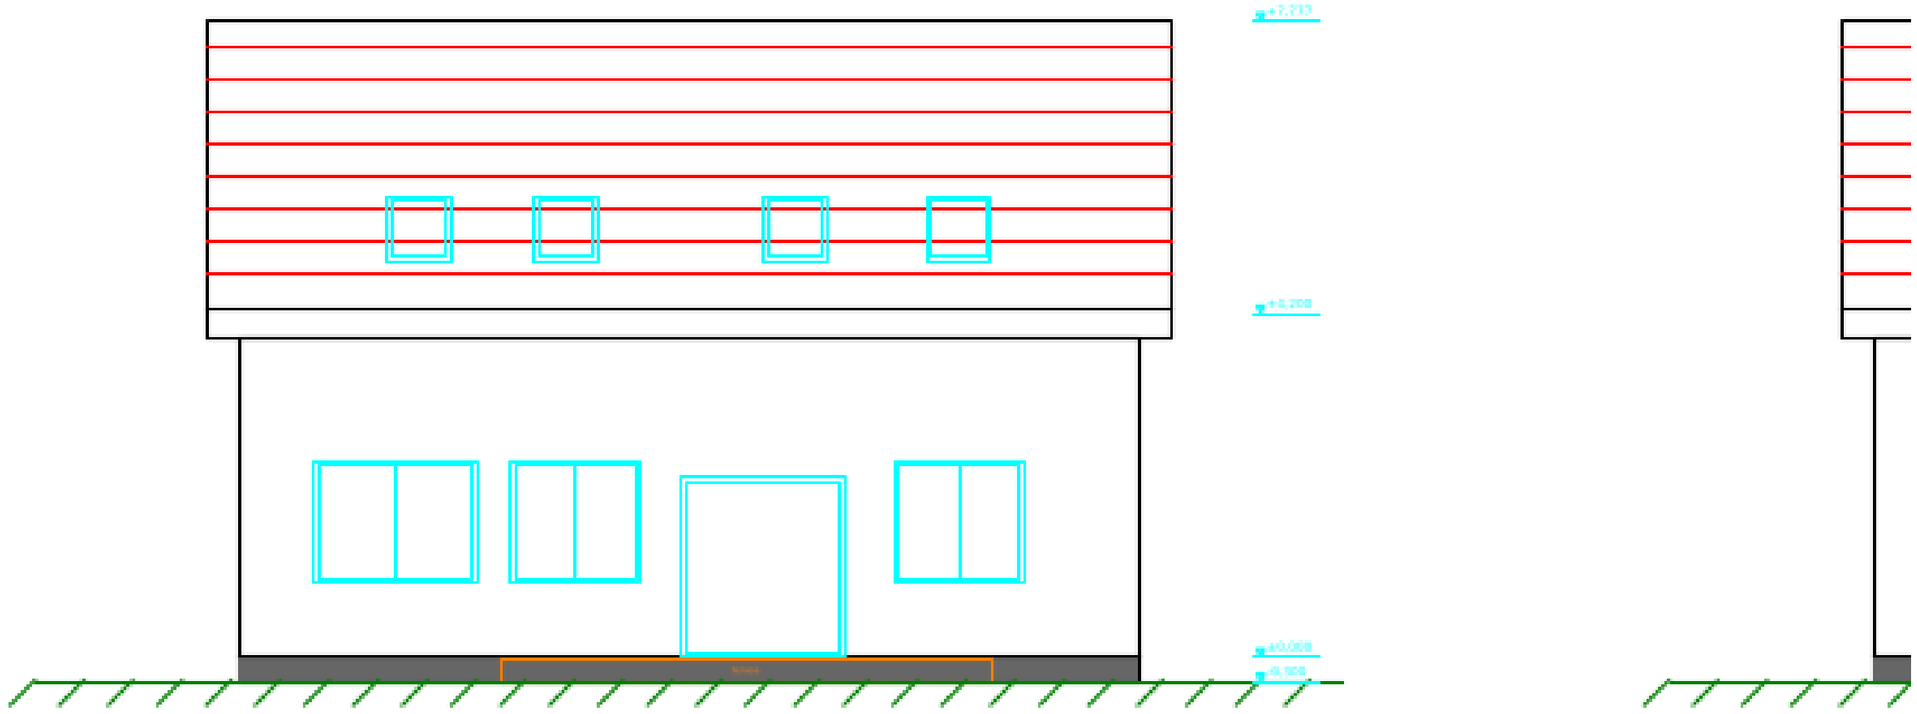


POHĽAD JUŽNÝ
M 1:50

RODINNÝ DOM – Pohľad severný

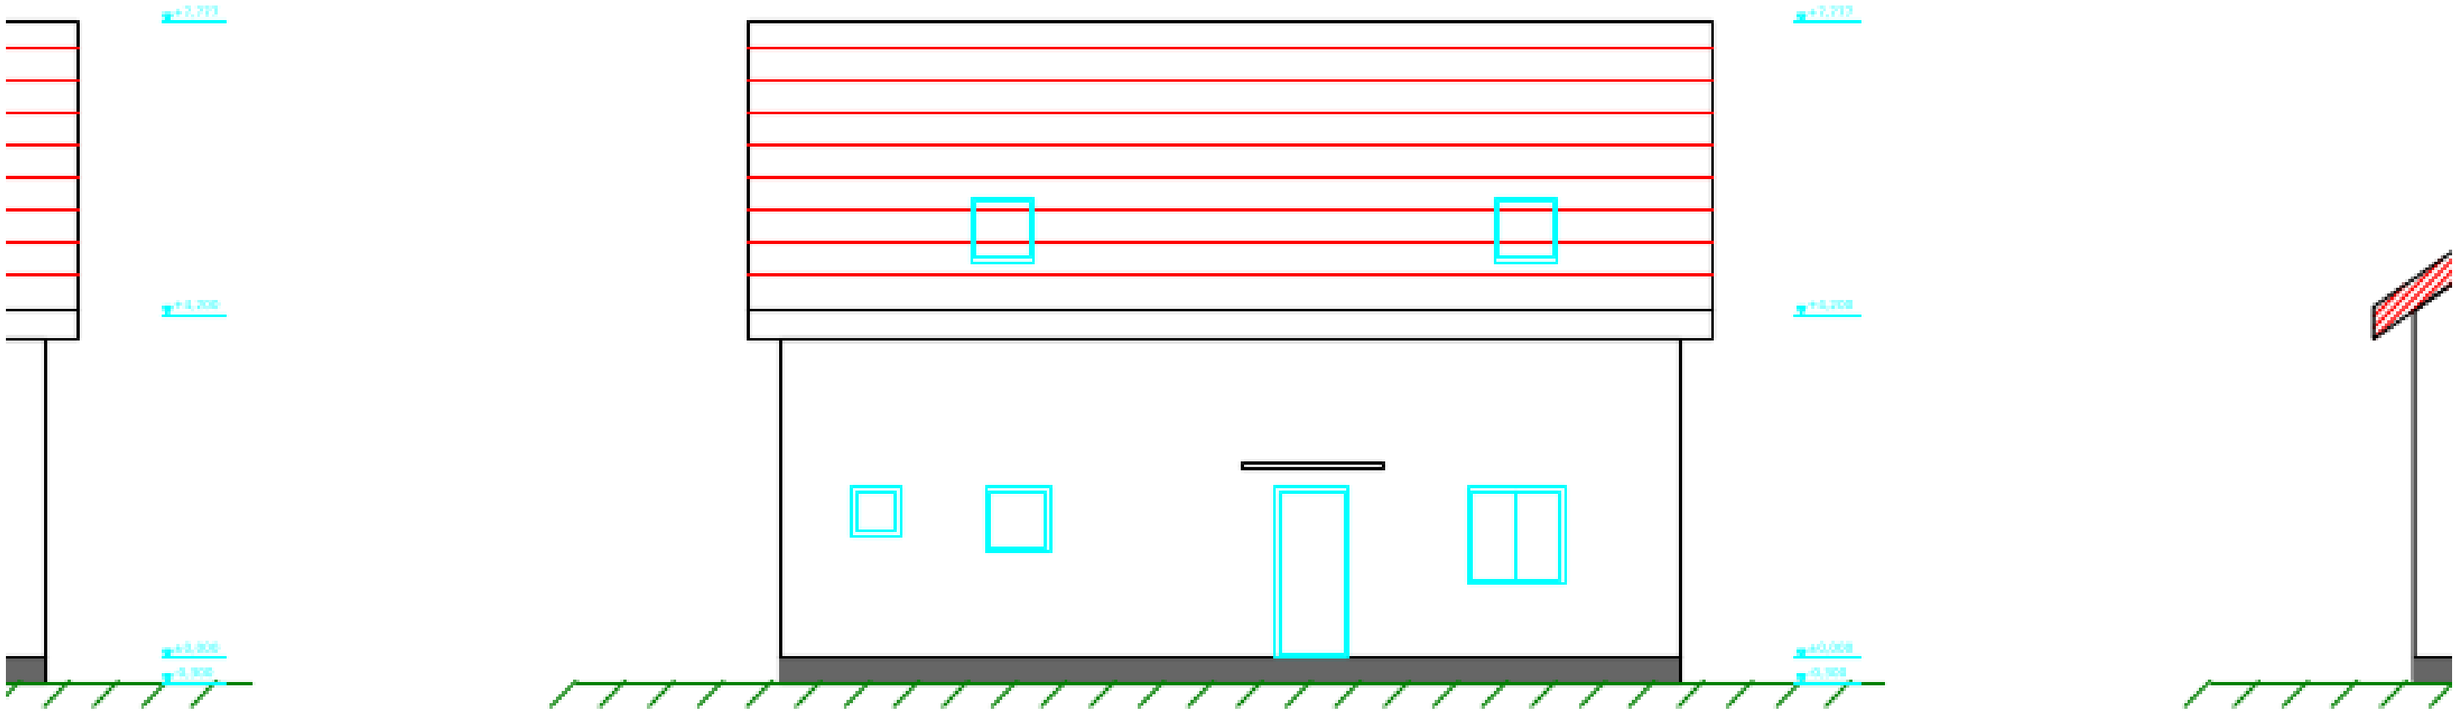


POHĽAD SEVERNÝ (od ulice)
M 1:50

RODINNÝ DOM – Pohľad východný

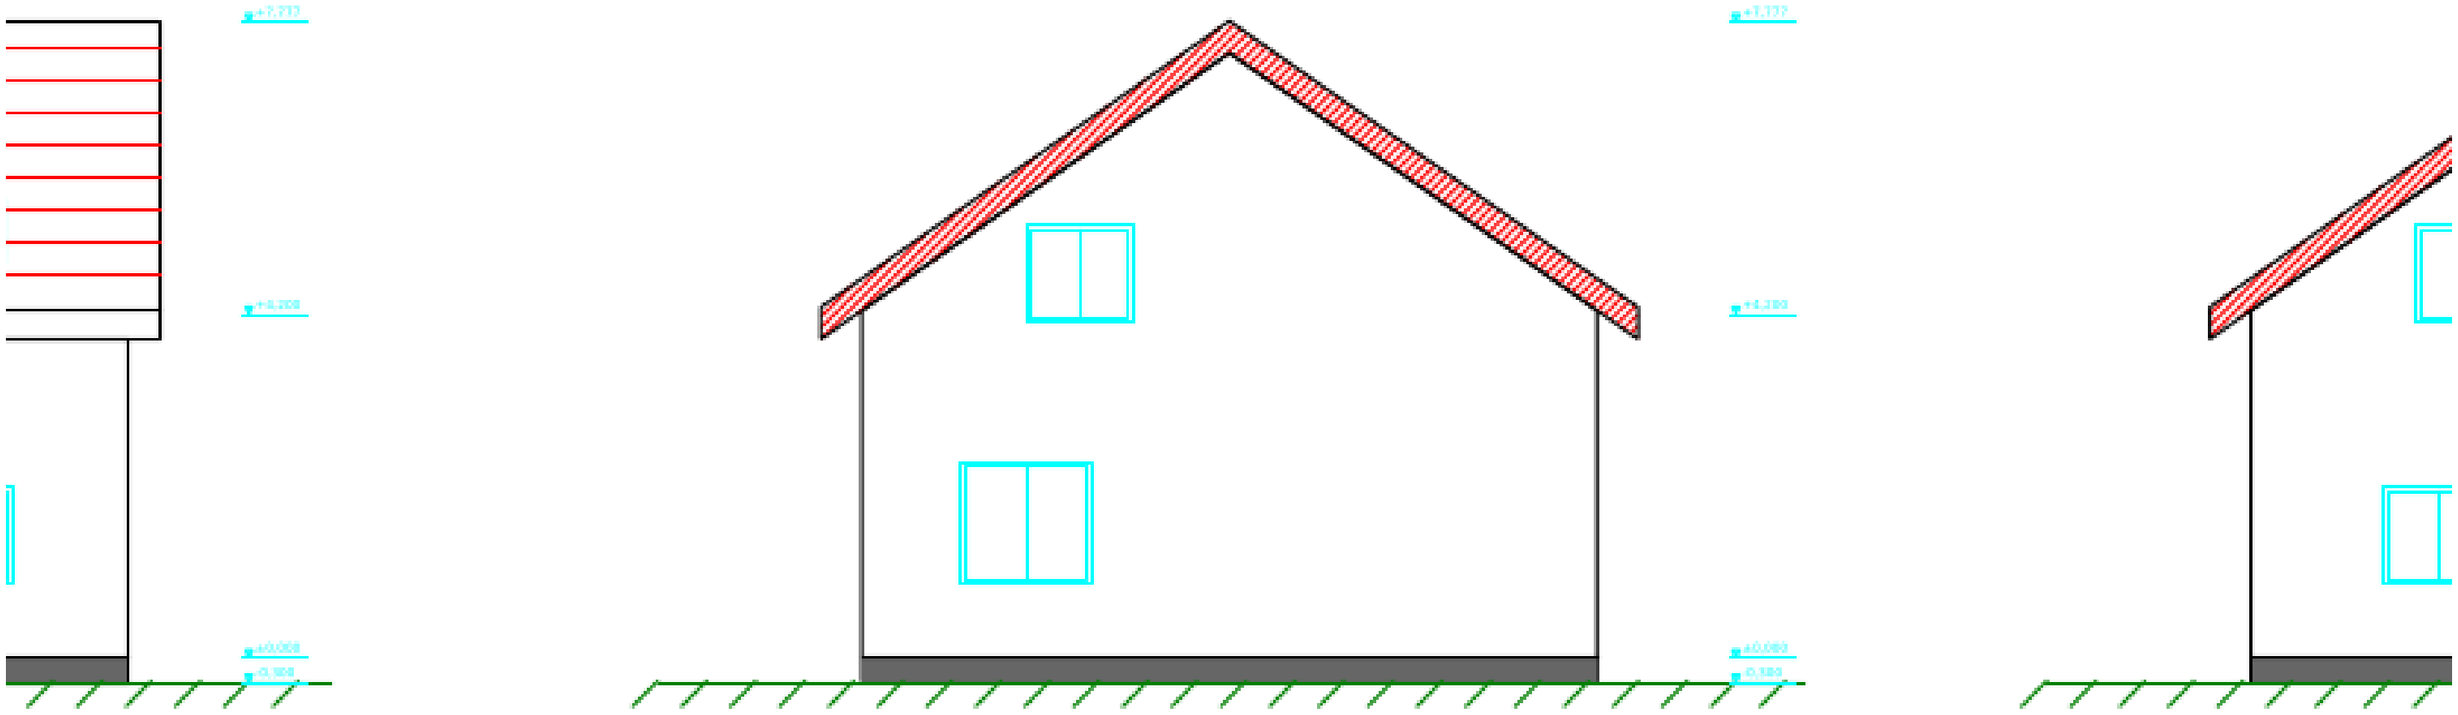

POHĽAD VÝCHODNÝ
M 1:50

RODINNÝ DOM – Pohľad západný

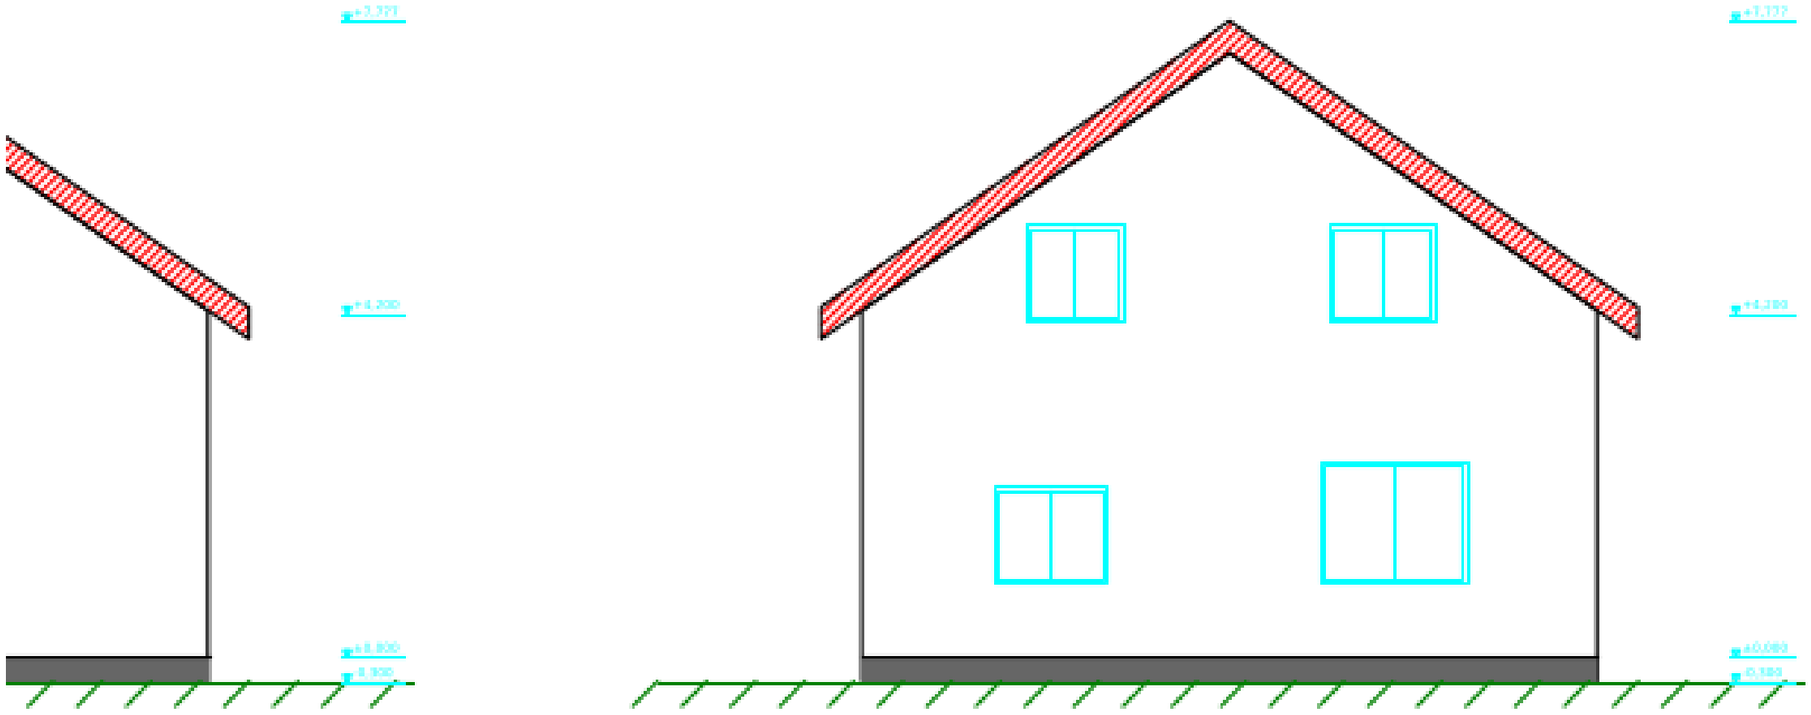

POHĽAD ZÁPADNÝ
M 1:50

POZNÁMKY, PREDPOKLADY A SKLADBY

PREDBEŽNÁ ARCHITEKTONICKÁ ŠTÚDIA – nie je projekt pre stavebné konanie.

Predpoklady (upraviť podľa skutočnosti):
• pozemok 20 × 30 m, rovinatý, ulica na severe, terasa a obytné miestnosti na juh,
• murovaný dom z tehly, sedlová strecha 35°, prízemie + obývané podkrovie, bez garáže,
• regulatívy územného plánu obce (zastavanosť, odstupy, výška, tvar strechy) treba overiť.

Nad rámec tejto štúdie – vypracujú autorizovaní projektanti:
• statika (základy, ŽB strop, krov) podľa STN EN 1990 – 1997,
• tepelnotechnické posúdenie a energetické hodnotenie (budova A0, STN 73 0540),
• požiarna bezpečnosť (STN 73 0802), ZTI, kúrenie, vetranie, elektro,
• geologický prieskum, radónové riziko, nepremŕzavá hĺbka.

Schodisko: 18 stupňov × 172 mm, šírka stupnice 265 mm, ramená 1000 mm (STN 73 4130 overiť).

Orientačné skladby (hrúbky izolácií určí energetický posudok):
Obvodová stena: omietka | EPS fasádny 150 | tehlový múr 300 | vnútorná omietka.
Podlaha na teréne: krytina + anhydrit 80 | EPS 120 | ŽB doska 150 | hydroizolácia | štrk 150.
Strop nad 1.NP: ŽB monolitická doska 250 + plávajúca podlaha podkrovia 100.
Strecha: škridla | latovanie + kontralatovanie | difúzna fólia | krokvy 100×200 s minerálnou vlnou medzi krokvami 200 + pod krokvami 60 | parozábrana | SDK 12,5.

